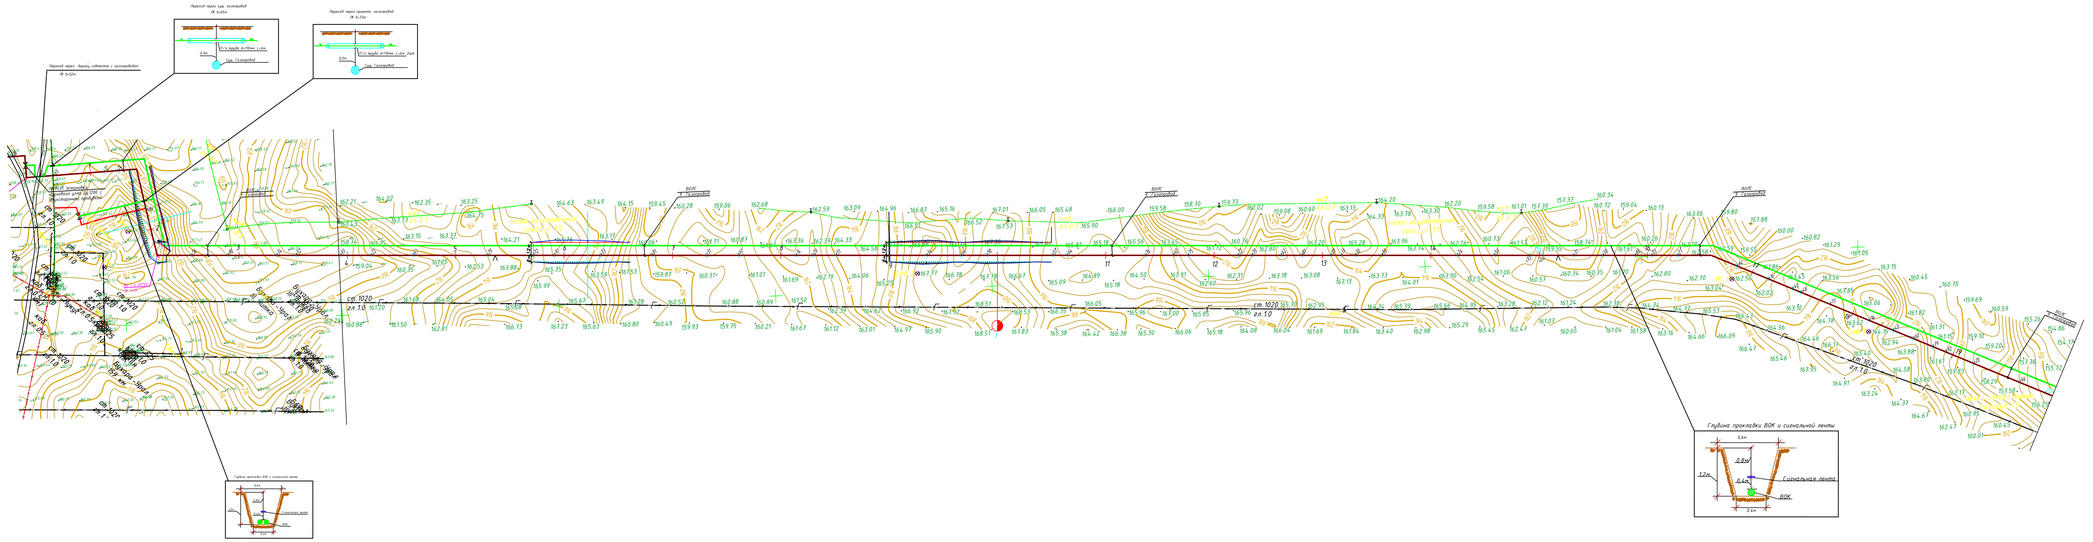

Переход через ул. Газопроводов
М 1:25 и
Переход через проезжую часть газопровод
М 1:25 и
Переход через дорогу собственных с газопроводом
М 1:500
ВОЛС
Газопровод
ПК 0+00
ПК 1+00
ПК 2+00
ПК 3+00
ПК 4+00
ПК 5+00
ПК 6+00
ПК 7+00
ПК 8+00
ПК 9+00
ПК 10+00
ПК 11+00
ПК 12+00
ПК 13+00
ПК 14+00
ПК 15+00
ПК 16+00
ПК 17+00
ПК 18+00
ПК 19+00
ПК 20+00
ул. Газопроводов
ул. Газопроводов
ул. Газопроводов