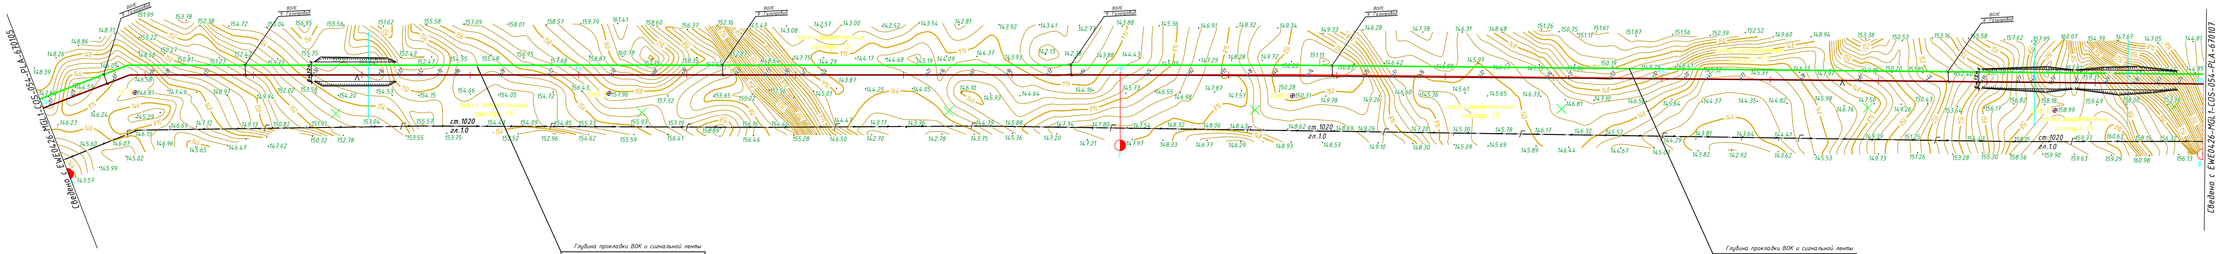
Схема расположения листов

COS-054-PLA-670105	COS-054-PLA-670106	COS-054-PLA-670107

Условные обозначения

- Столбик
- Маркер
- Соединительная муфта
- Проектируемый волоконно-оптический кабель
- Проектный Газопровод
- Существующий Газопровод


Сведено с EWE0426-MGL1-COS-054-PLA-670106
Сведено с EWE0426-MGL1-COS-054-PLA-670107
ВОЛС
Сигнальная лента
ст.1020
ел.1.0
Кабель оптический
Кабель оптический
Кабель оптический