Схема расположения листов

COS-054-PLA-670107	▨ COS-054-PLA-670108	COS-054-PLA-670109

Условные обозначения

⅄	Столбик
●	Маркер
—(M)—	Соединительная муфта
🟩	Проектируемый волоконно-оптический кабель
🟥	Проектный Газопровод
—г—г—	Существующий Газопровод

Сведено с EWE0426-MGL1-COS-054-PLA-670107
ВОЛС
9 Газопровод
ст.1020
гл.1.0
Сведено с EWE0426-MGL1-COS-054-PLA-670109

Глубина прокладки ВОК и сигнальной ленты

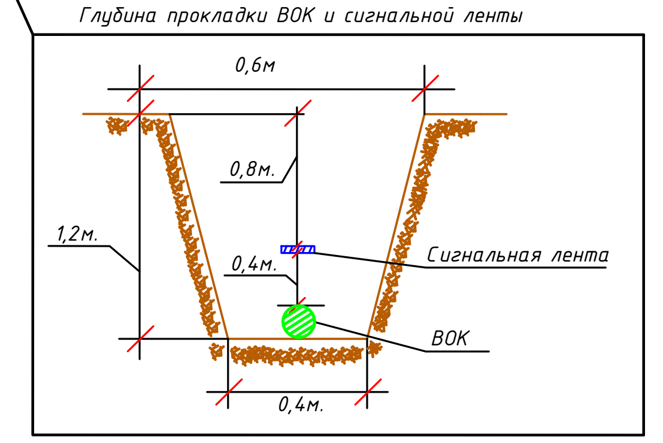

Глубина прокладки ВОК и сигнальной ленты

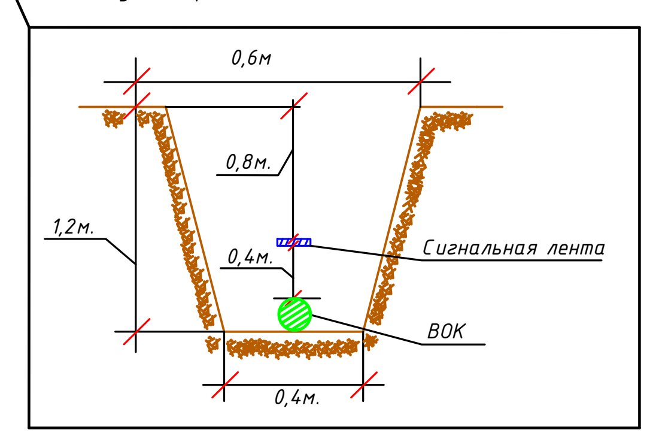

1 Общие данные - чертеж EWE0426-MGL1-COS-054-COM-670101

2.Структурная схема см. EWE0426-MGL1-COS-054-SCM-670102

3 Прокладка ВОЛС на существующих площадках и подключения к существующим и проектируемым объектам будут показаны после предоставления исходных данных

4 Расстановка муфт, маркеров, замерных столбиков будут показаны после предоставления исходных данных и расстановки технологических площадок.

Рев.	Дата	Назначение ревизии	Проверил	Утвердил
A1	20.07.2026	Выпущено для строительства		
R1	03.07.2026	Выпущено для рассмотрения		

ЗАКАЗЧИК: UZTRANSGAZ
ГЕНЕРАЛЬНЫЙ ПОДРЯДЧИК: UZBEKENERGOTAMIR
ПОДРЯДЧИК: PBG Pro Build Generation
ГЕНЕРАЛЬНЫЙ ПРОЕКТИРОВЩИК: EAST WEST ENGINEERING

EWE0426-MGL1-COS-054-PLA-670108-A1

Строительство новых ниток (участков) газопроводов «Газли - Саримой» и «Акчалок - Газли - Нукус» общей протяженностью не менее 275 км

Изм.	Кол. уч	Лист	№док.	Подп.	Дата
ГИП		Схабицкий А.			20.07.26
Нач. отд.		Кабулова Е.		Кабулова	20.07.26
Исполн.		Кабулова Е.		Кабулова	20.07.26
Н.контр.		Схабицкий А.			20.07.26

Газопровод Газли-Сарымай (54км)
ВОЛС

Стадия	Лист	Листов
РД	1	1

Ситуационный план
ПК100+00- ПК120+00

ООО "EAST-WEST Engineering"
г. Ташкент 2026г.

Формат А3Х4 / Format A3X4

Взам. инв. №

Подпись и дата

Инв.№ подл.