
Ситуационная схема прокладки кабеля ВОЛС

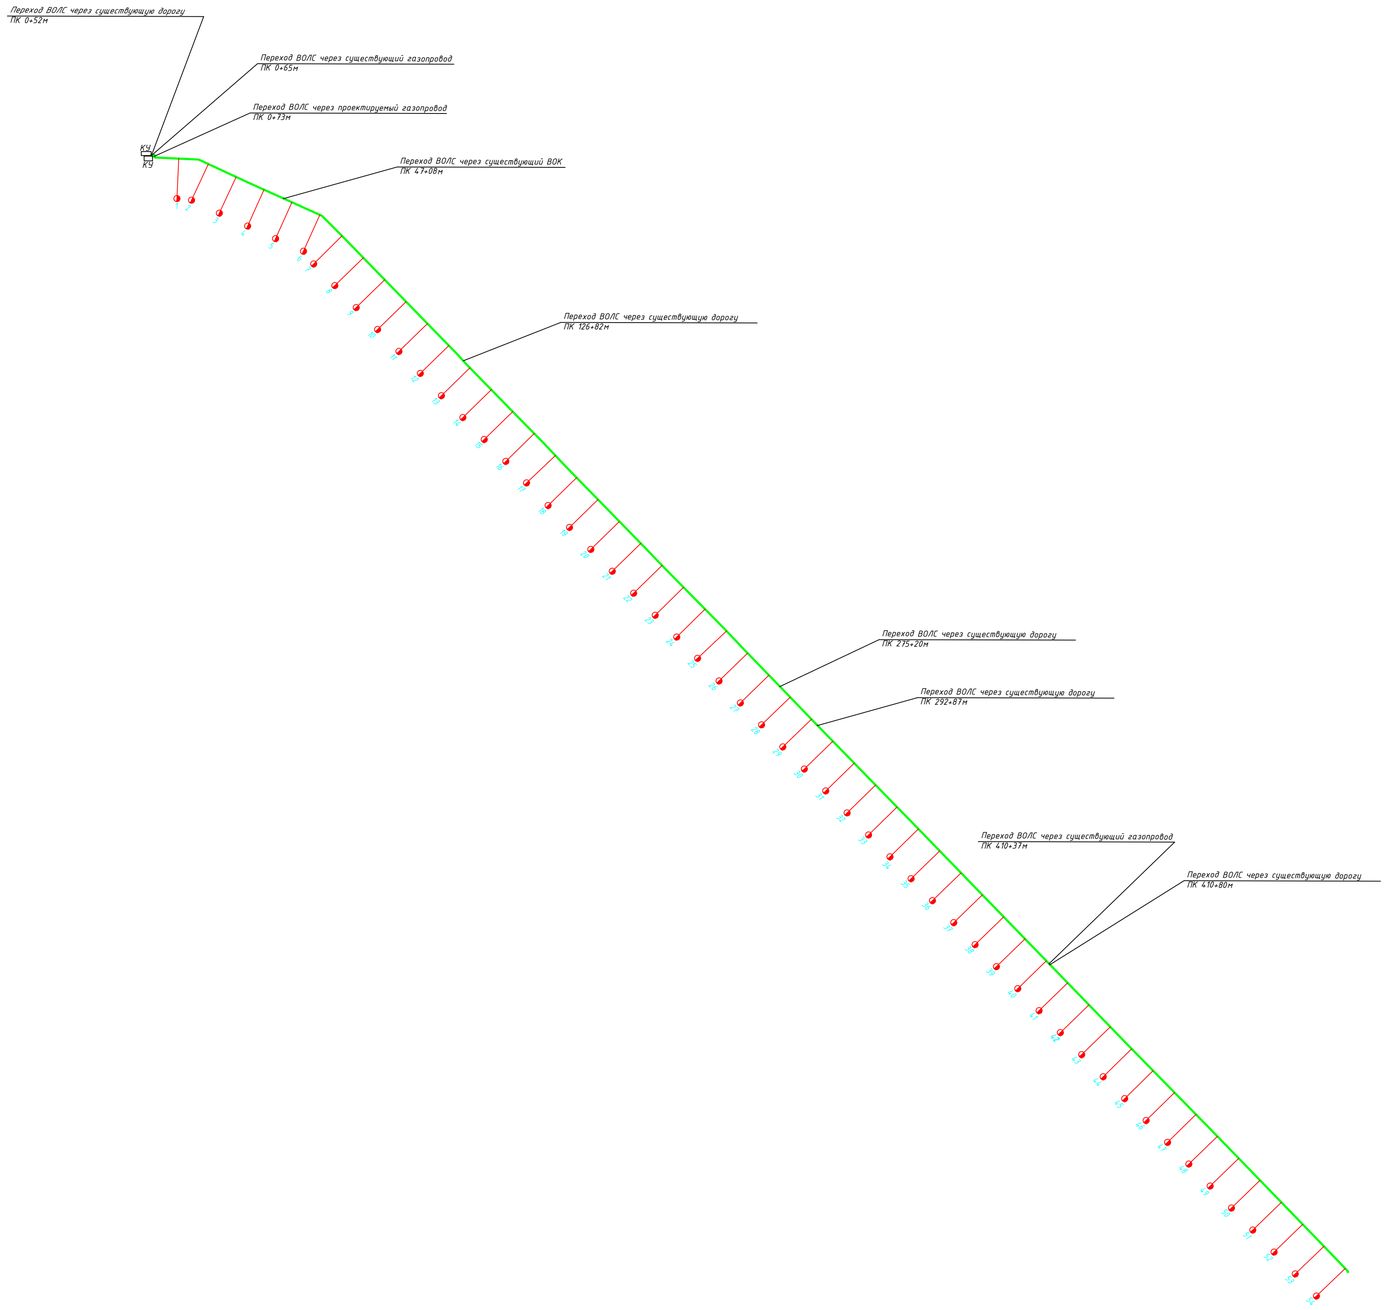

Условные обозначения

- Волоконно оптический кабель
- Пикет
- Соединительная муфта (M)

1 Общие данные - чертеж EWE0426-MGL1-COS-054-COM-670101
2 Прокладка ВОЛС на существующих площадках и подключения к существующим и проектируемым объектам будут показаны после предоставления исходных данных
3 Расстановка муфт будет показана после предоставления исходных данных и расстановки технологических площадок.

Рев.	Дата	Назначение ревизии	Проверил	Утвердил
A1	20.07.2026	Выпущено для строительства		
R1	03.07.2026	Выпущено для рассмотрения		

ЗАКАЗЧИК: UTG | ГЕНЕРАЛЬНЫЙ ПОДРЯДЧИК: UET | ПОДРЯДЧИК: PBG | ГЕНЕРАЛЬНЫЙ ПРОЕКТИРОВЩИК: EAST WEST ENGINEERING

Изм.	Кол. уч.	Лист	№док.	Подп.	Дата	EWE0426-MGL1-COS-054-SCM-670102-A1		
						Строительство новых ниток (участков) газопроводов «Газли - Саримой» и «Акчалок - Газли - Нукус» общей протяженностью не менее 275 км		
ГИП		Скавицкий А.			20.07.26	Газопровод Газли-Сарымай (54км) ВОЛС	Стадия: РД	Лист: 1 / Листов: 1
Нач. отд.		Кабулова Е.			20.07.26			
Исполн.		Кабулова Е.			20.07.26			
Н.контр.		Скавицкий А.			20.07.26	Структурная схема	EAST WEST ENGINEERING	ООО "EAST-WEST Engineering" г. Ташкент 2026г.

Взам. инв. №
Подпись и дата
Инв.№ подл.

Формат A1 / Format A1